FRONT ELEVATION

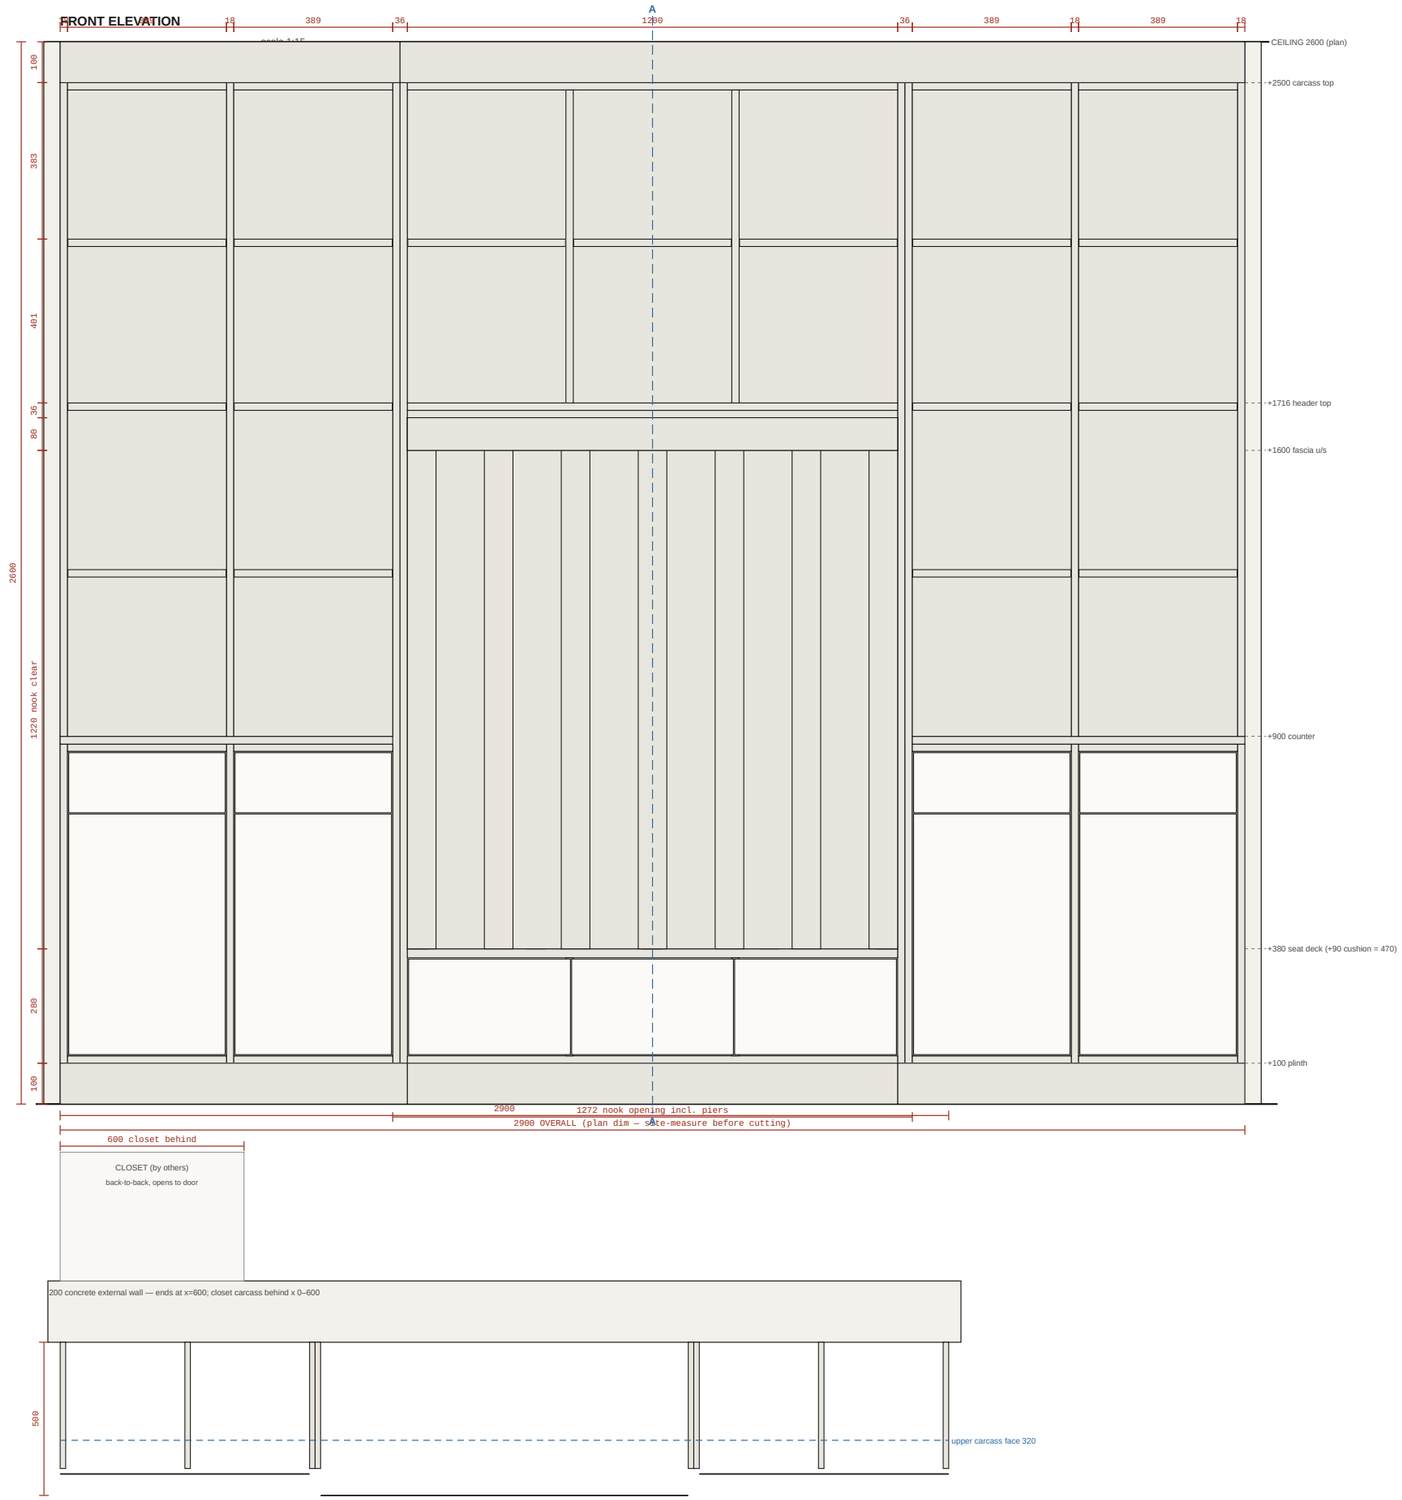

SECTION A–A through the nook · 1:15

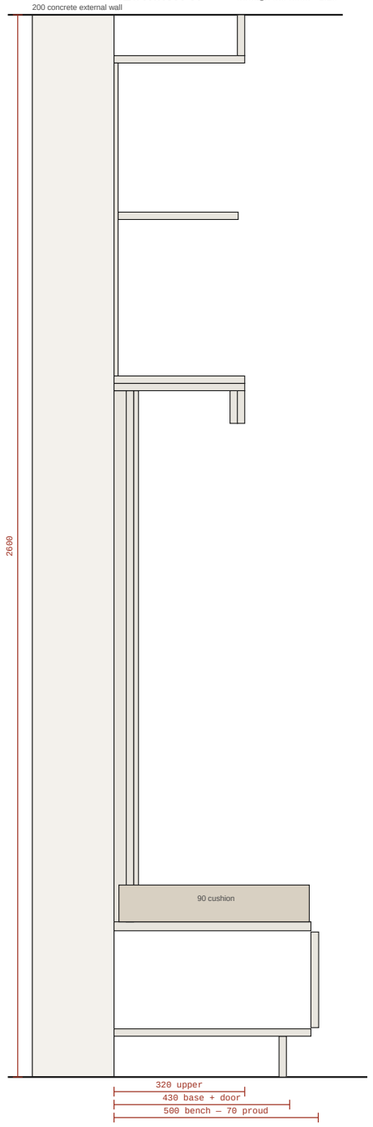

CRITICAL NOTES

1. ALL DIMENSIONS IN MILLIMETRES. Drawing is PROVISIONAL — 2900 and 2600 are architect's plan dimensions, NOT site-measured. Before any cutting: measure the opening width at floor / 900 / ceiling and the height at left / centre / right, take both diagonals, and build to the SMALLEST reading. Surplus goes into the scribe.
2. HEADER. The 1200 span is the one part of this design that fails slowly and permanently. 36mm flat (2×18 laminated) sags 9.8mm over time under a book load. The 80mm fascia glued AND screwed to the front edge makes it an L-beam — 1.2mm. Do not omit the fascia. Do not substitute a single 18mm deck.
3. BENCH DECK is 22mm over TWO mullions. 18mm over one mullion deflects 4.8mm under an 80kg adult. Do not substitute 18mm.
4. PIERS are 2×18 laminated to 36mm, full height 100–2500, and carry the header and the whole upper centre. Glue the full face, not just the edges.
5. No vertical panel lands on the wall/closet junction at x=600 — it falls inside bay 2. The bookcase carcass is self-supporting; the closet is a separate box behind.
6. FIXING is into 200mm concrete: M8 sleeve or chemical anchors. Have the plumber mark the 4" drain stack on the wall before drilling. Anti-tip fixing is mandatory.
7. BACKS sit in a 4mm dado, not on cam fittings. Upper backs are VISIBLE inside the open shelving — 10mm MDF, sprayed both faces.
8. NO EDGE BANDING. All MDF edges are sealed, filled and sprayed.
9. SCRIBE 15mm at the right-hand end against the wall. Left end is an exposed finished return beside the door.
10. EXISTING OUTLET, low and central, lands behind the bench drawers. A live box may NOT be buried behind fixed joinery with no access. The nook back is therefore furred 30mm off the concrete to form a SERVICE VOID: the relocated socket and both sconces wire through it with NO chasing of the external wall, and the existing box stays reachable by pulling the centre bench drawer out. Cut the boxes on site, after the חשמלאי sets the positions.

MAIN-ROOM NOOK UNIT — ספרים עם גומחת ישיבה	יחידת
UNITS mm	**DO NOT CUT FROM THIS DRAWING UNTIL THE WALL IS MEASURED**
SCALE 1:15 elev+sect, 1:20 plan @ A3	
MATERIAL MDF, sprayed — routed shaker fronts	
STATUS DRAFT — 13 decisions open, not site-measured	
PARTS 104 pieces / 31 line items	